



COLUMN RFT PART  
5 1 : 25



01 8R8-L=1.97 m@100 m

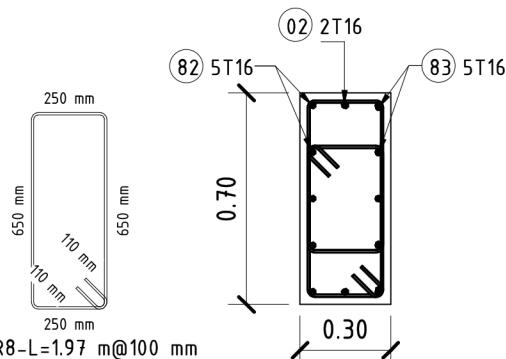

COLUMN RFT SEC 1-1  
1 : 25

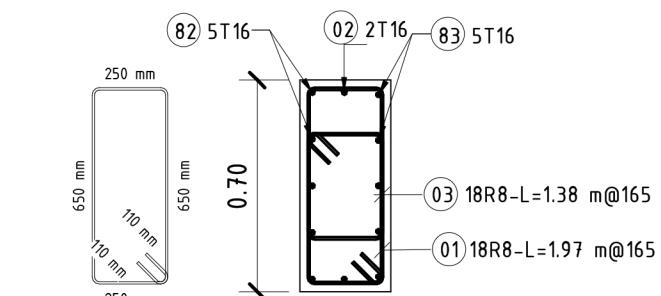

01 18R8-L=1.97 m@165 mm

0.30

250 mm


353 mm

110 mm


110 mm

353 mm

250 mm

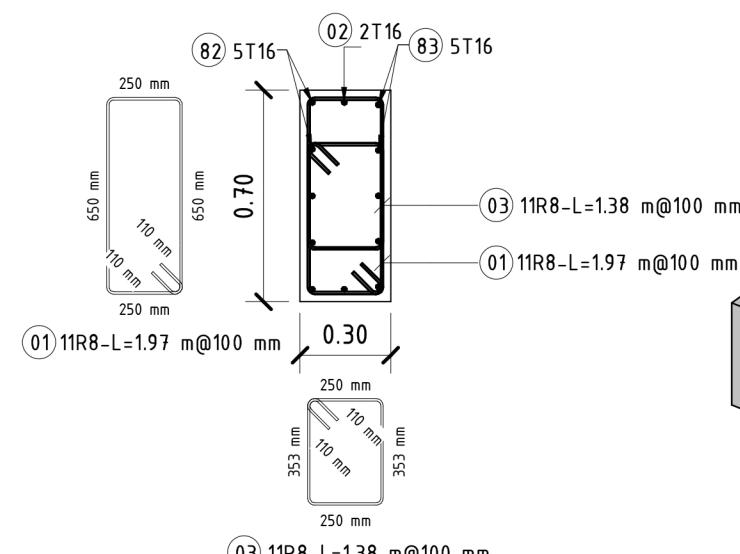

COLUMN RFT SEC 3-3  
3 1 : 25

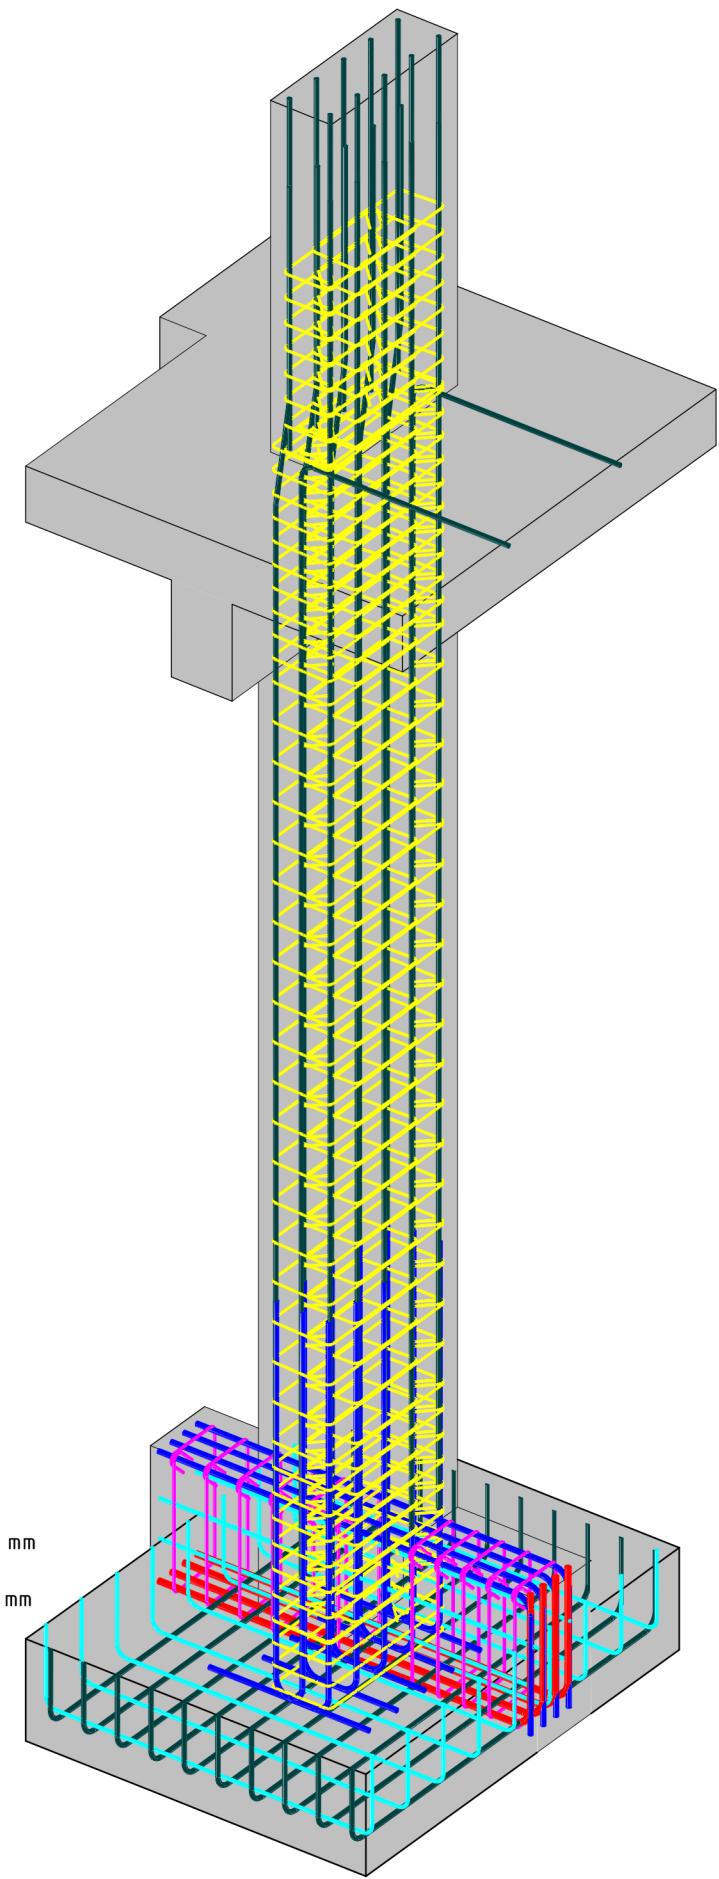

## COLUMN PART 1 3D